
1:25 1.25m 1 0.75 0.5 0.25 0 1:50 2.5m 2 1.5 1 0.5 0

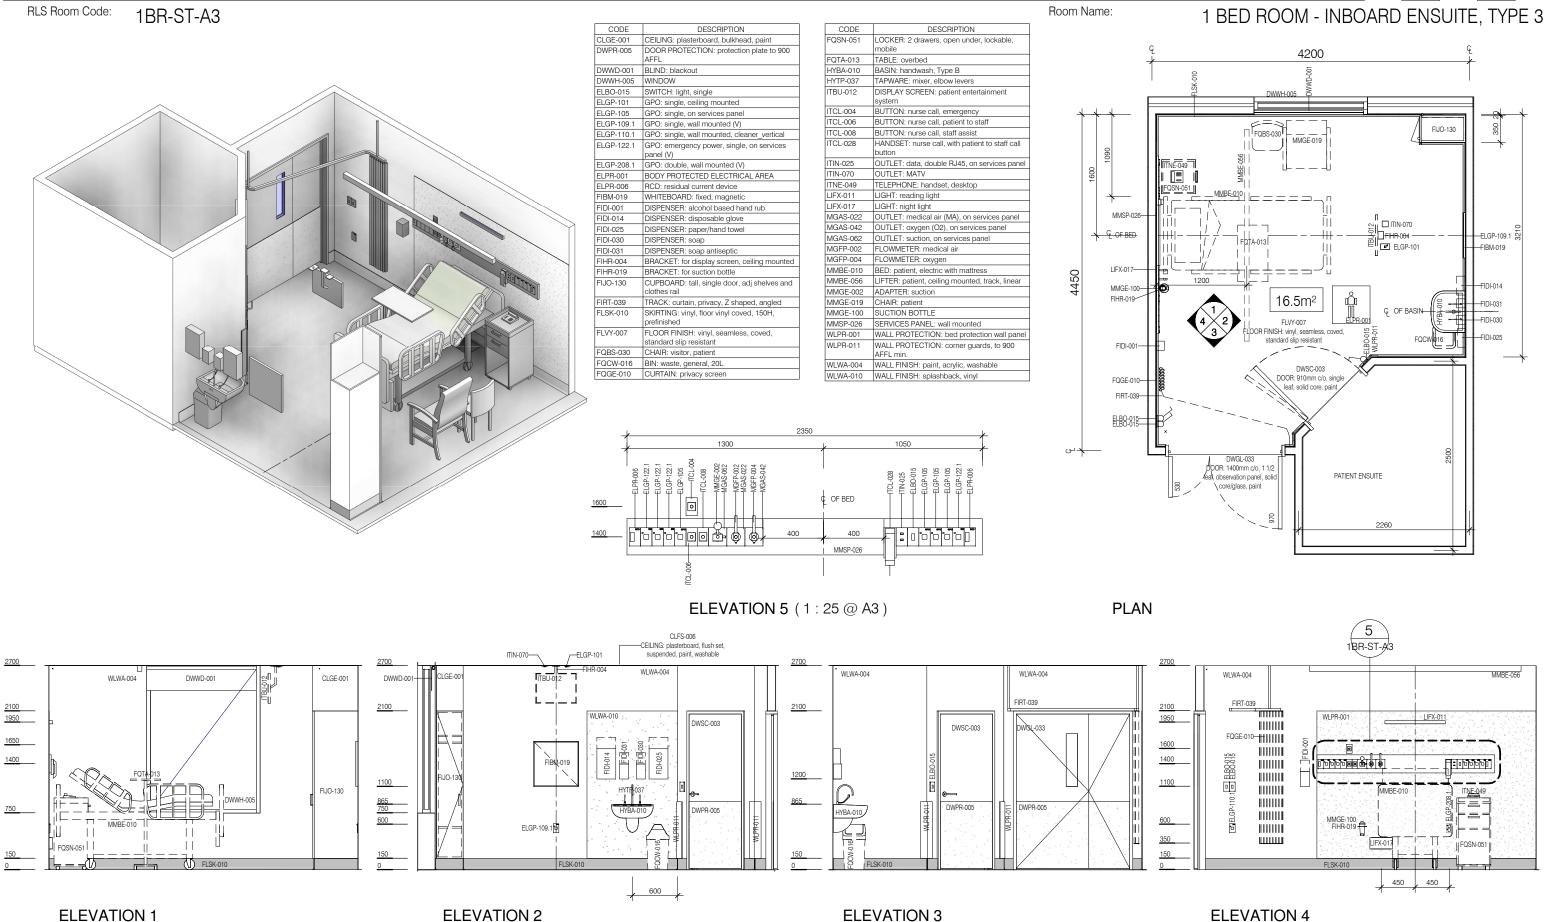

	Australasian Health Facility Guidelines
	Australasian Health Facility Guidelines

REV	DESCRIPTION	DATE
2	Notes added	15.08.2005
3	Updated following ERG Review	05.04.2018

FOR GUIDANCE

SCALE	RLS Room Code	REV
1 : 50 @ A3	1BR-ST-A3	3