
RLS Room Code: 1BR-ST-B3

Room Name:

1 BED ROOM - OUTBOARD ENSUITE, TYPE 3


0.75_

1:25 1.25m_

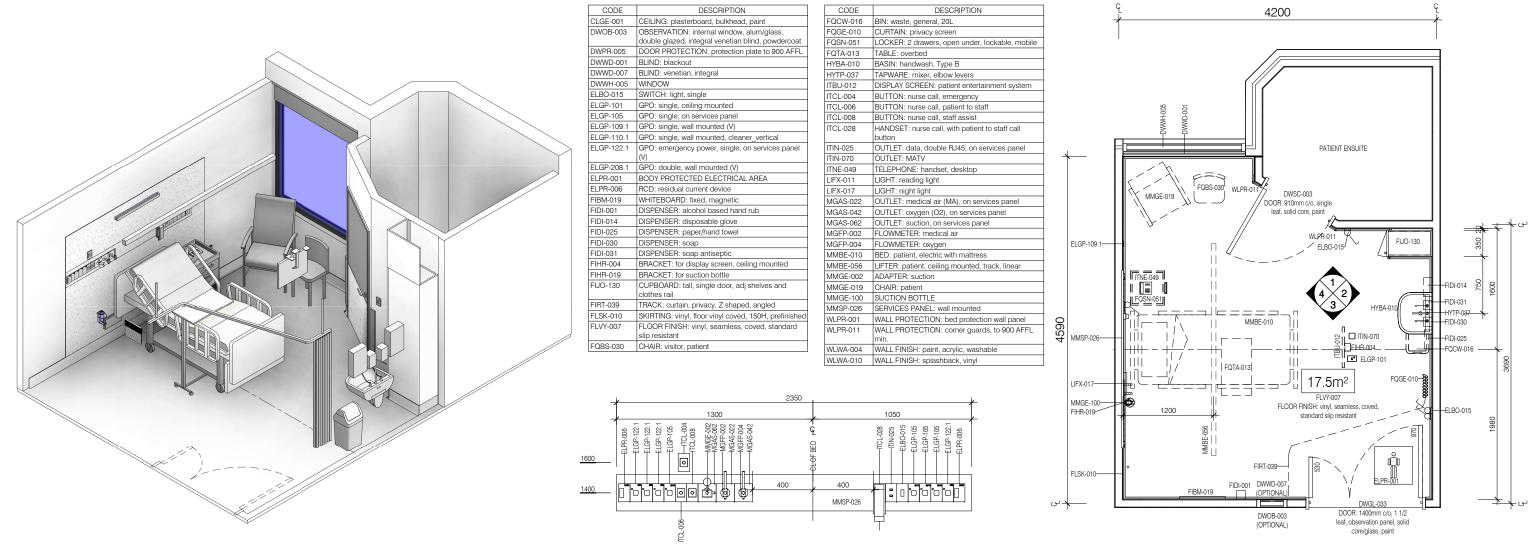

ELEVATION 5 (1:25 @ A3)

PLAN

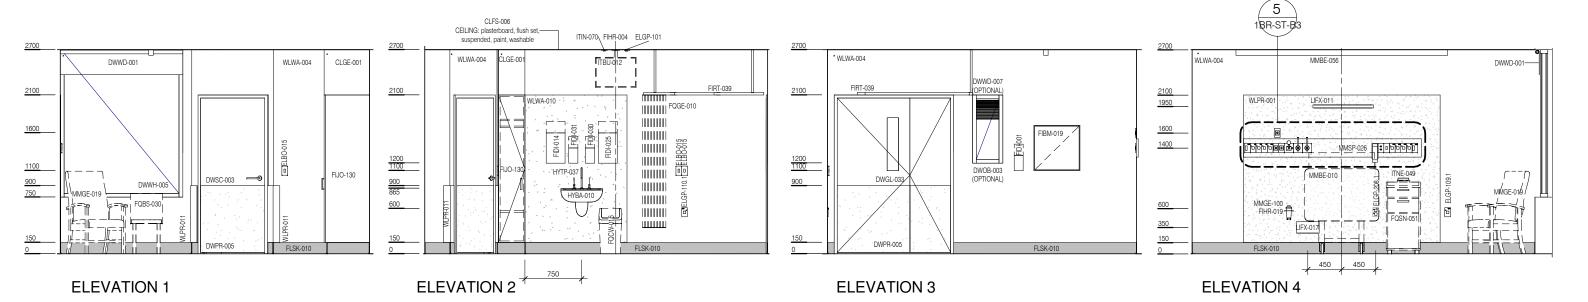

٨٠٠٠
Australasian Health Facility Guidelines

REV	DESCRIPTION	DATE
1	Updated following ERG Review	05.04.2018

FOR GUIDANCE

SCALE	RLS Room Code	REV
1 : 50 @ A3	1BR-ST-B3	1