
RLS Room Code:

1BR-SP-A2

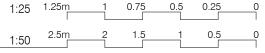

FQBS-055

MMGE-019

FIDI-031-

Room Name: 1 BED ROOM - SPECIAL, INBOARD ENSUITE, TYPE 2

MMSP-026

LIFX-017


MMGE-100-


€ OF BED


4200

18.0m²

FLOOR FINISH: vinvl. seamless, coved

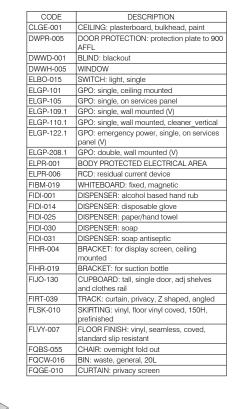


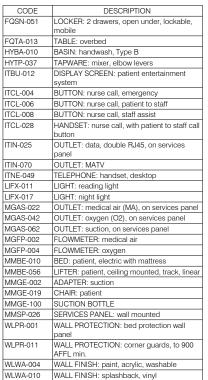

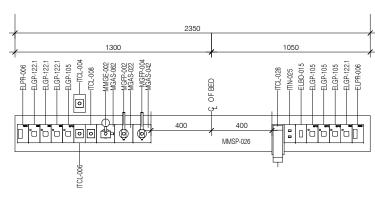

FIDI-001-FQCW-016— FQGE-010 DWSC-003 DOOR: 910mm c/o, single ELGP-110.1leaf, solid core FIRT-039-ELBO-015— ELBO-015— DWGL-033 DOOR: 1400mm c/o, 1 1/2 PATIENT ENSUITE core/glass, paint **PLAN**

ELEVATION 5 (1:25 @ A3)

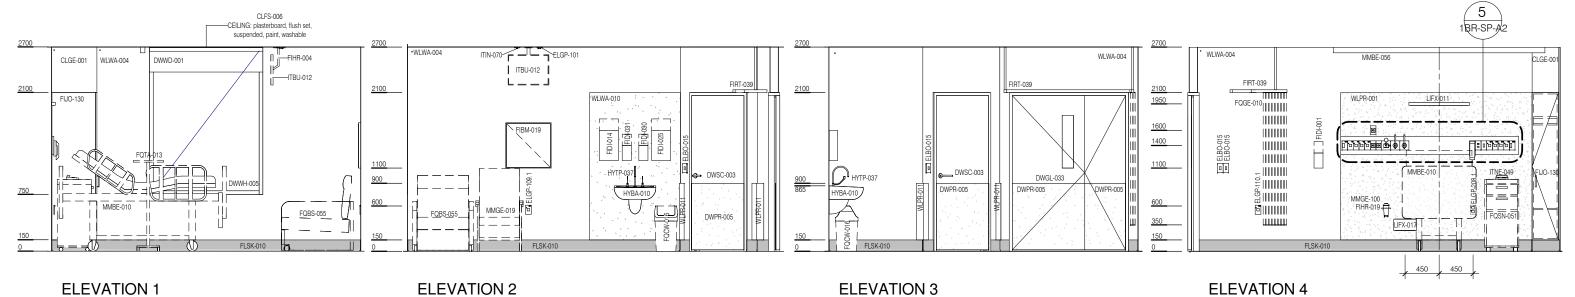

Australosion Health Facility Guidelines

REV	DESCRIPTION	DATE
1	Updated following ERG Review	05.04.2018

SCALE	RLS Room Code	REV
1 : 50 @ A3	1BR-SP-A2	1