
RLS Room Code:

1BR-ST-B2




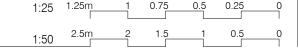


1 BED ROOM - OUTBOARD ENSUITE, TYPE 2

0.75\_




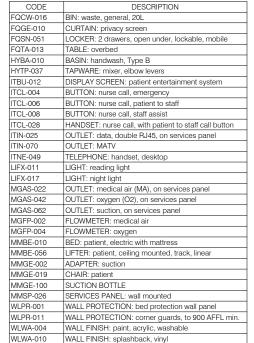

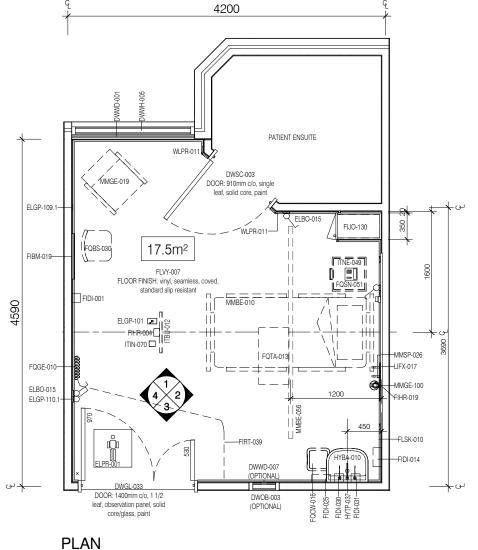

1300 1050 0

**ELEVATION 5** (1:25 @ A3)

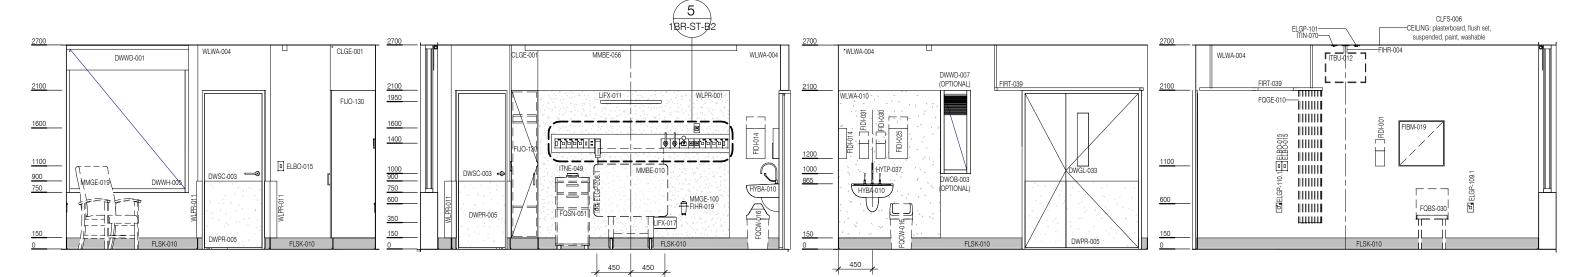

**ELEVATION 1 ELEVATION 2 ELEVATION 3 ELEVATION 4** 



REV	DESCRIPTION	DATE
1	Updated following ERG Review	05.04.2018

FOR GUIDANCE

SCALE	RLS Room Code	REV
1 : 50 @ A3	1BR-ST-B2	1