
Room Layout Sheet

1:25 1.25m 1 0.75 0.5 0.25 0 1:50 2.5m 2 1.5 1 0.5 0

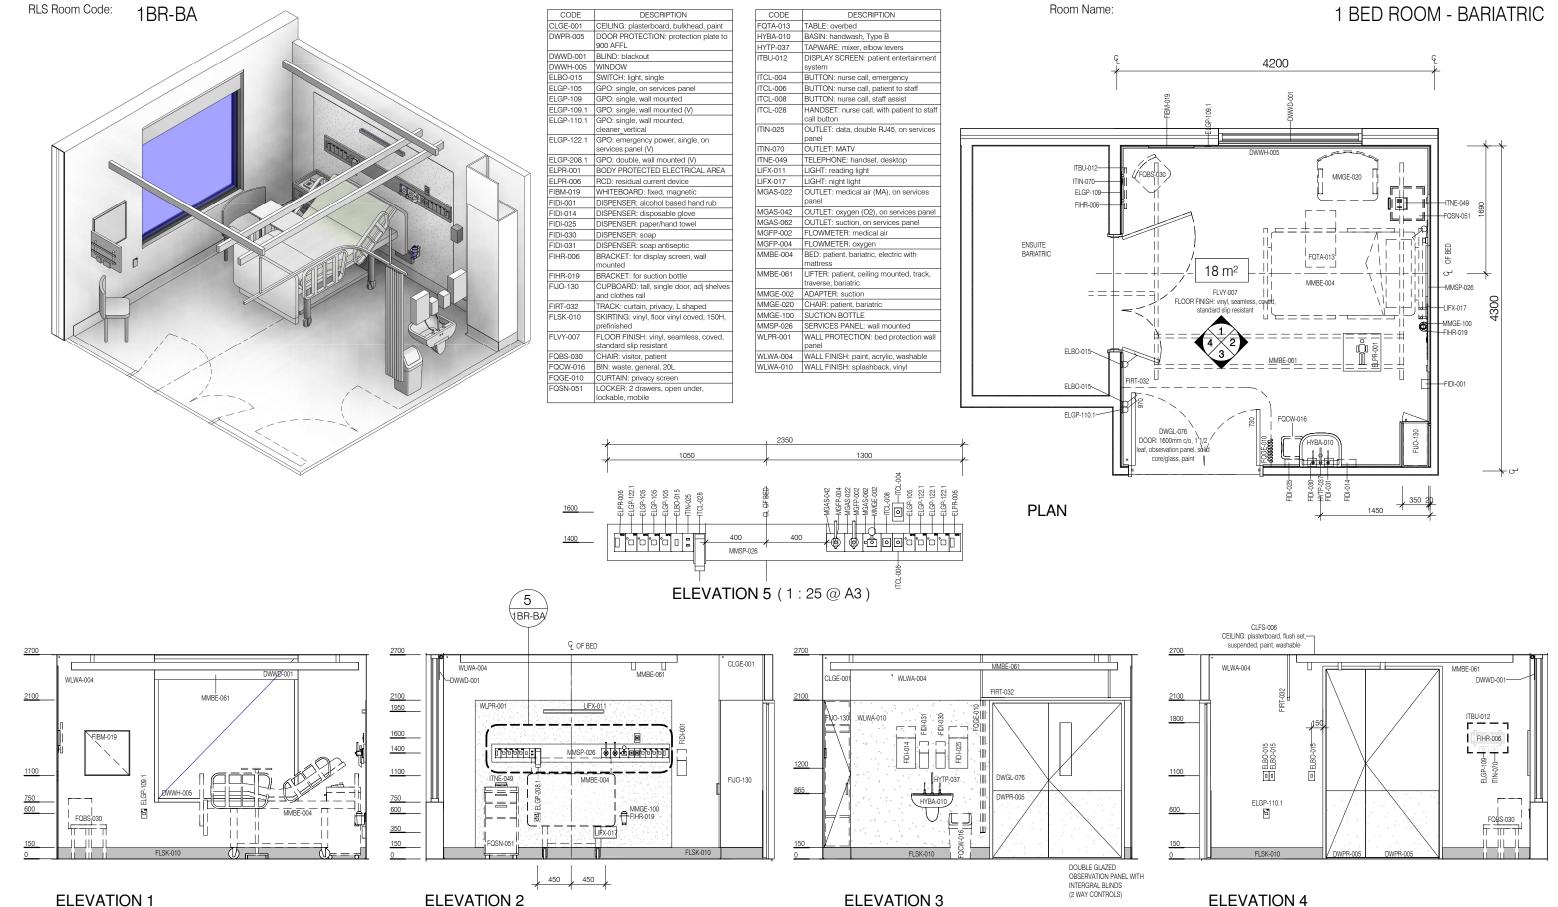



REV	DESCRIPTION	DATE
1	Updated following ERG Review	05.04.2018

FOR GUIDANCE

SCALE	RLS Room Code	REV
1 : 50 @ A3	1BR-BA	1