AUSTRALASIAN HFG STANDARD COMPONENTS

Room Layout Sheet

RLS Room Code: AMBTR

Room Name: AMBULANCE TRIAGE

1:50 2.5m 2 1.5 1 0.5 0

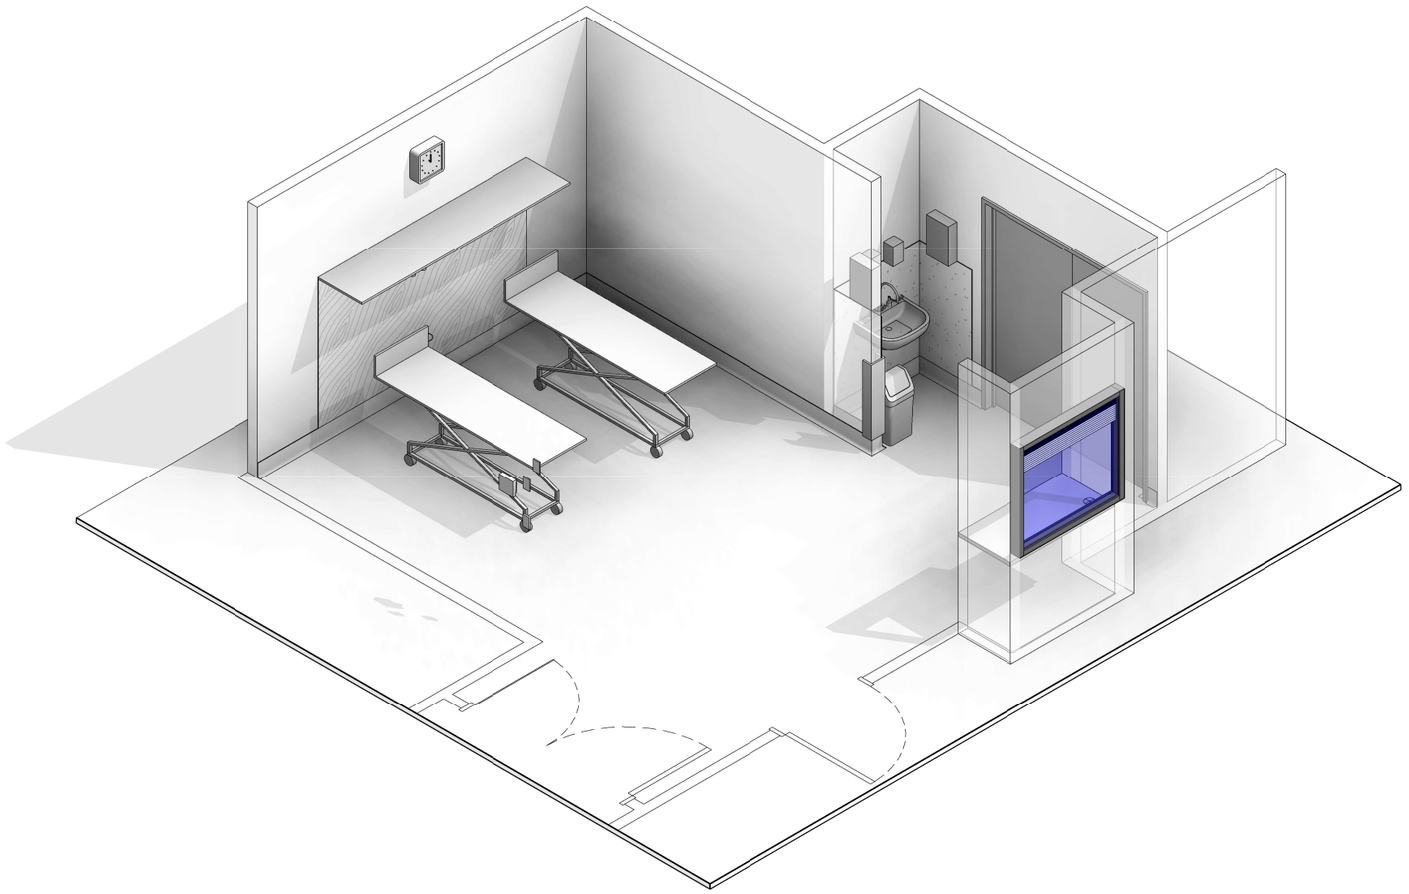

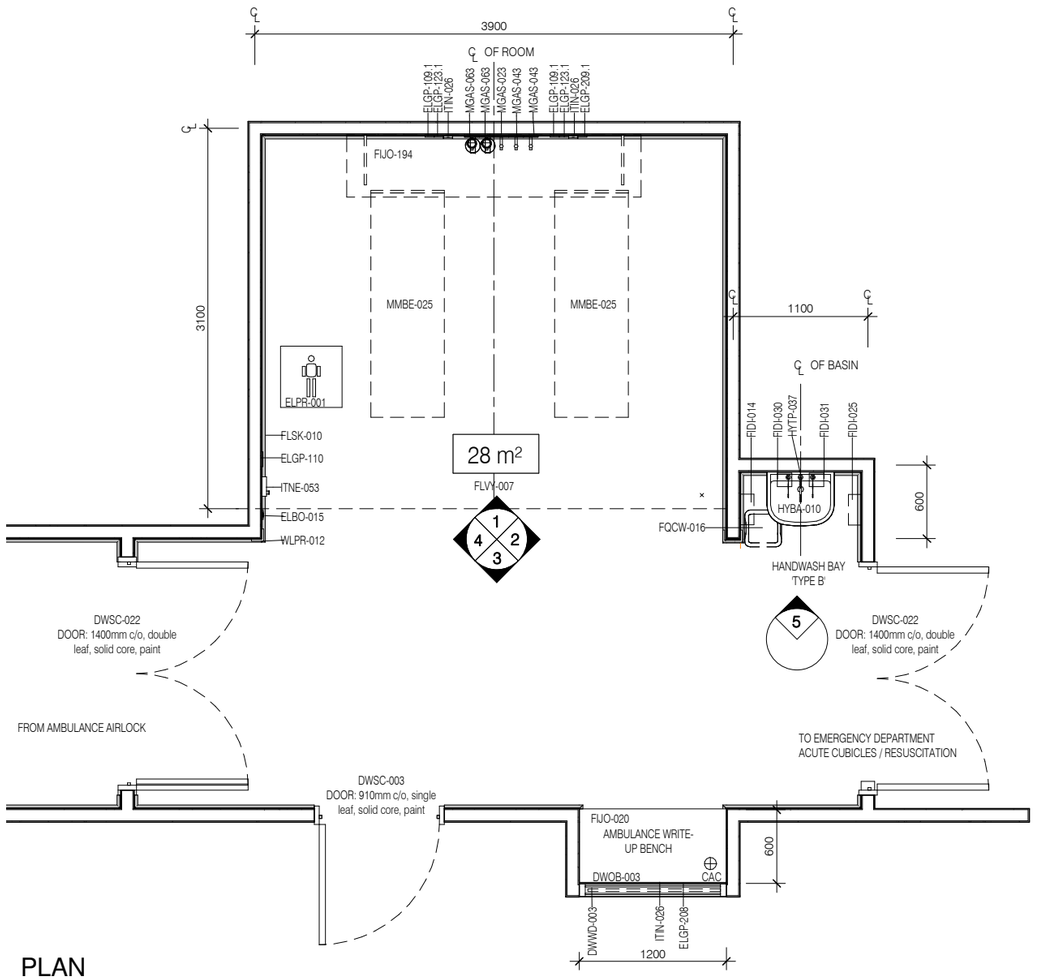

PLAN

CODE	DESCRIPTION
CAC	Cable access cap
DWOB-003	OBSERVATION: internal window, alum/glass, double glazed, integral venetian blind, powdercoat
DWWD-003	BLIND: integral
ELBO-015	SWITCH: light, single
ELGP-109.1	GPO: single, wall mounted (V)
ELGP-110	GPO: single, wall mounted, cleaner
ELGP-123.1	GPO: emergency power, single, wall mounted (V)
ELGP-208	GPO: double, wall mounted
ELGP-209.1	GPO: double, wall mounted, RCD protected (V)
ELPR-001	BODY PROTECTED ELECTRICAL AREA
FIDI-014	DISPENSER: disposable glove
FIDI-025	DISPENSER: paper/hand towel
FIDI-030	DISPENSER: soap
FIDI-031	DISPENSER: soap antiseptic
FIHR-019	BRACKET: for suction bottle
FIJO-020	BENCH: 600D, open under, laminate finish
FIJO-194	SHELF: laminate
FLSK-010	SKIRTING: vinyl, floor vinyl coved, 150H, prefinished
FLVY-007	FLOOR FINISH: vinyl, seamless, coved, standard slip resistant

CODE	DESCRIPTION
FQCW-016	BIN: waste, general, 20L
FQGE-005	CLOCK: analogue, battery operated
HYBA-010	BASIN: handwash, Type B
HYTP-037	TAPWARE: mixer, elbow levers
ITCL-004	BUTTON: nurse call, emergency
ITCL-008	BUTTON: nurse call, staff assist
ITIN-026	OUTLET: data, double RJ45, wall mounted
ITNE-053	TELEPHONE: handset, wall mount, handsfree
MGAS-023	OUTLET: medical air (MA), wall mounted
MGAS-043	OUTLET: oxygen (O2), wall mounted
MGAS-063	OUTLET: suction, wall mounted
MGFP-002	FLOWMETER: medical air
MGFP-004	FLOWMETER: oxygen
MMBE-025	GURNEY
MMGE-002	ADAPTER: suction
MMGE-100	SUCTION BOTTLE
WLPR-002	WALL PROTECTION: bed protection wall panel, composite, laminate finish
WLPR-012	WALL PROTECTION: corner guards, to 900 AFFL, prefinished PVC
WLWA-004	WALL FINISH: paint, acrylic, washable
WLWA-010	WALL FINISH: splashback, vinyl

AustHFG Australasian Health Facility Guidelines

REV	DESCRIPTION	DATE
3	Coding and naming updated	20.03.2017

FOR GUIDANCE

SCALE	RLS Room Code	REV
1 : 50 @ A3	AMBTR	3

AUSTRALASIAN HFG STANDARD COMPONENTS

Room Layout Sheet

RLS Room Code: AMBTR

Room Name: AMBULANCE TRIAGE

1:25 1.25m 1 0.75 0.5 0.25 0

1:50 2.5m 2 1.5 1 0.5 0

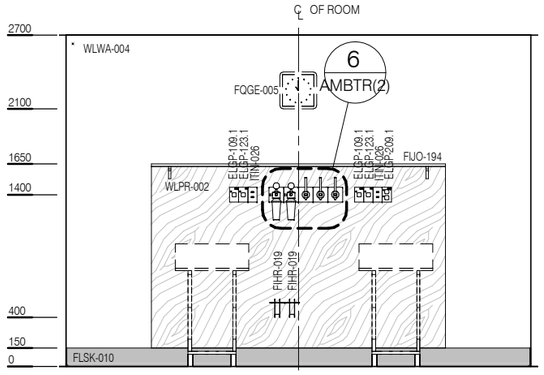

ELEVATION 1

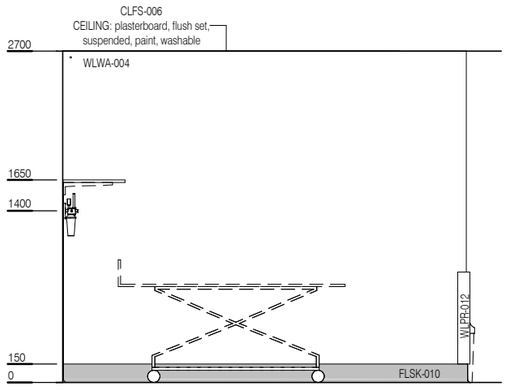

ELEVATION 2

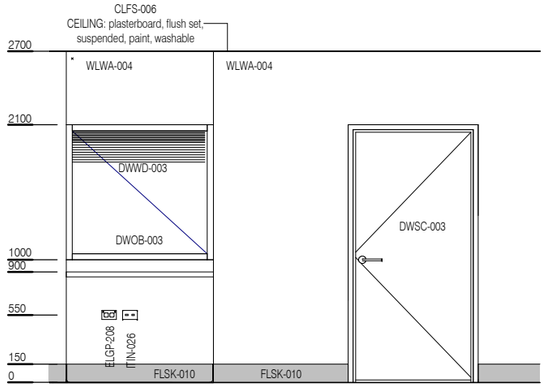

ELEVATION 3

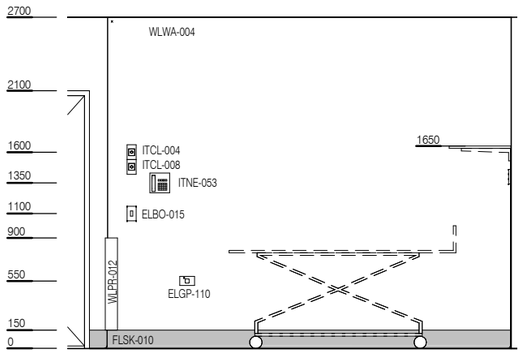

ELEVATION 4

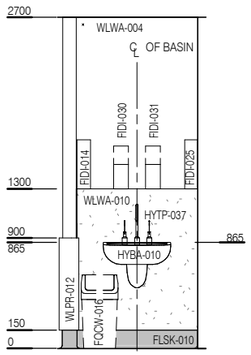

ELEVATION 5

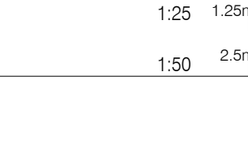

OPTIONAL MEDICAL GASES PANEL

ELEVATION 6 (1 : 25 @ A3)

CODE	DESCRIPTION
CAC	Cable access cap
DWOB-003	OBSERVATION: internal window, alum/glass, double glazed, integral venetian blind, powdercoat
DWWD-003	BLIND: integral
ELBO-015	SWITCH: light, single
ELGP-109.1	GPO: single, wall mounted (V)
ELGP-110	GPO: single, wall mounted, cleaner
ELGP-123.1	GPO: emergency power, single, wall mounted (V)
ELGP-208	GPO: double, wall mounted
ELGP-209.1	GPO: double, wall mounted, RCD protected (V)
ELPR-001	BODY PROTECTED ELECTRICAL AREA
FIDI-014	DISPENSER: disposable glove
FIDI-025	DISPENSER: paper/hand towel
FIDI-030	DISPENSER: soap
FIDI-031	DISPENSER: soap antiseptic
FIHR-019	BRACKET: for suction bottle
FIJO-020	BENCH: 600D, open under, laminate finish
FIJO-194	SHELF: laminate
FLSK-010	SKIRTING: vinyl, floor vinyl coved, 150H, prefinished
FLVY-007	FLOOR FINISH: vinyl, seamless, coved, standard slip resistant
FQCW-016	BIN: waste, general, 20L

CODE	DESCRIPTION
FQGE-005	CLOCK: analogue, battery operated
HYBA-010	BASIN: handwash, Type B
HYTP-037	TAPWARE: mixer, elbow levers
ITCL-004	BUTTON: nurse call, emergency
ITCL-008	BUTTON: nurse call, staff assist
ITIN-026	OUTLET: data, double RJ45, wall mounted
ITNE-053	TELEPHONE: handset, wall mount, handsfree
MGAS-023	OUTLET: medical air (MA), wall mounted
MGAS-043	OUTLET: oxygen (O2), wall mounted
MGAS-063	OUTLET: suction, wall mounted
MGFP-002	FLOWMETER: medical air
MGFP-004	FLOWMETER: oxygen
MMBE-025	GURNEY
MMGE-002	ADAPTER: suction
MMGE-100	SUCTION BOTTLE
WLPR-002	WALL PROTECTION: bed protection wall panel, composite, laminate finish
WLPR-012	WALL PROTECTION: corner guards, to 900 AFFL, prefinished PVC
WLWA-004	WALL FINISH: paint, acrylic, washable
WLWA-010	WALL FINISH: splashback, vinyl

AusHFG Australasian Health Facility Guidelines

REV	DESCRIPTION	DATE
3	Coding and naming updated	20.03.2017

FOR GUIDANCE

SCALE	RLS Room Code	REV
1 : 50 @ A3	AMBTR	3